

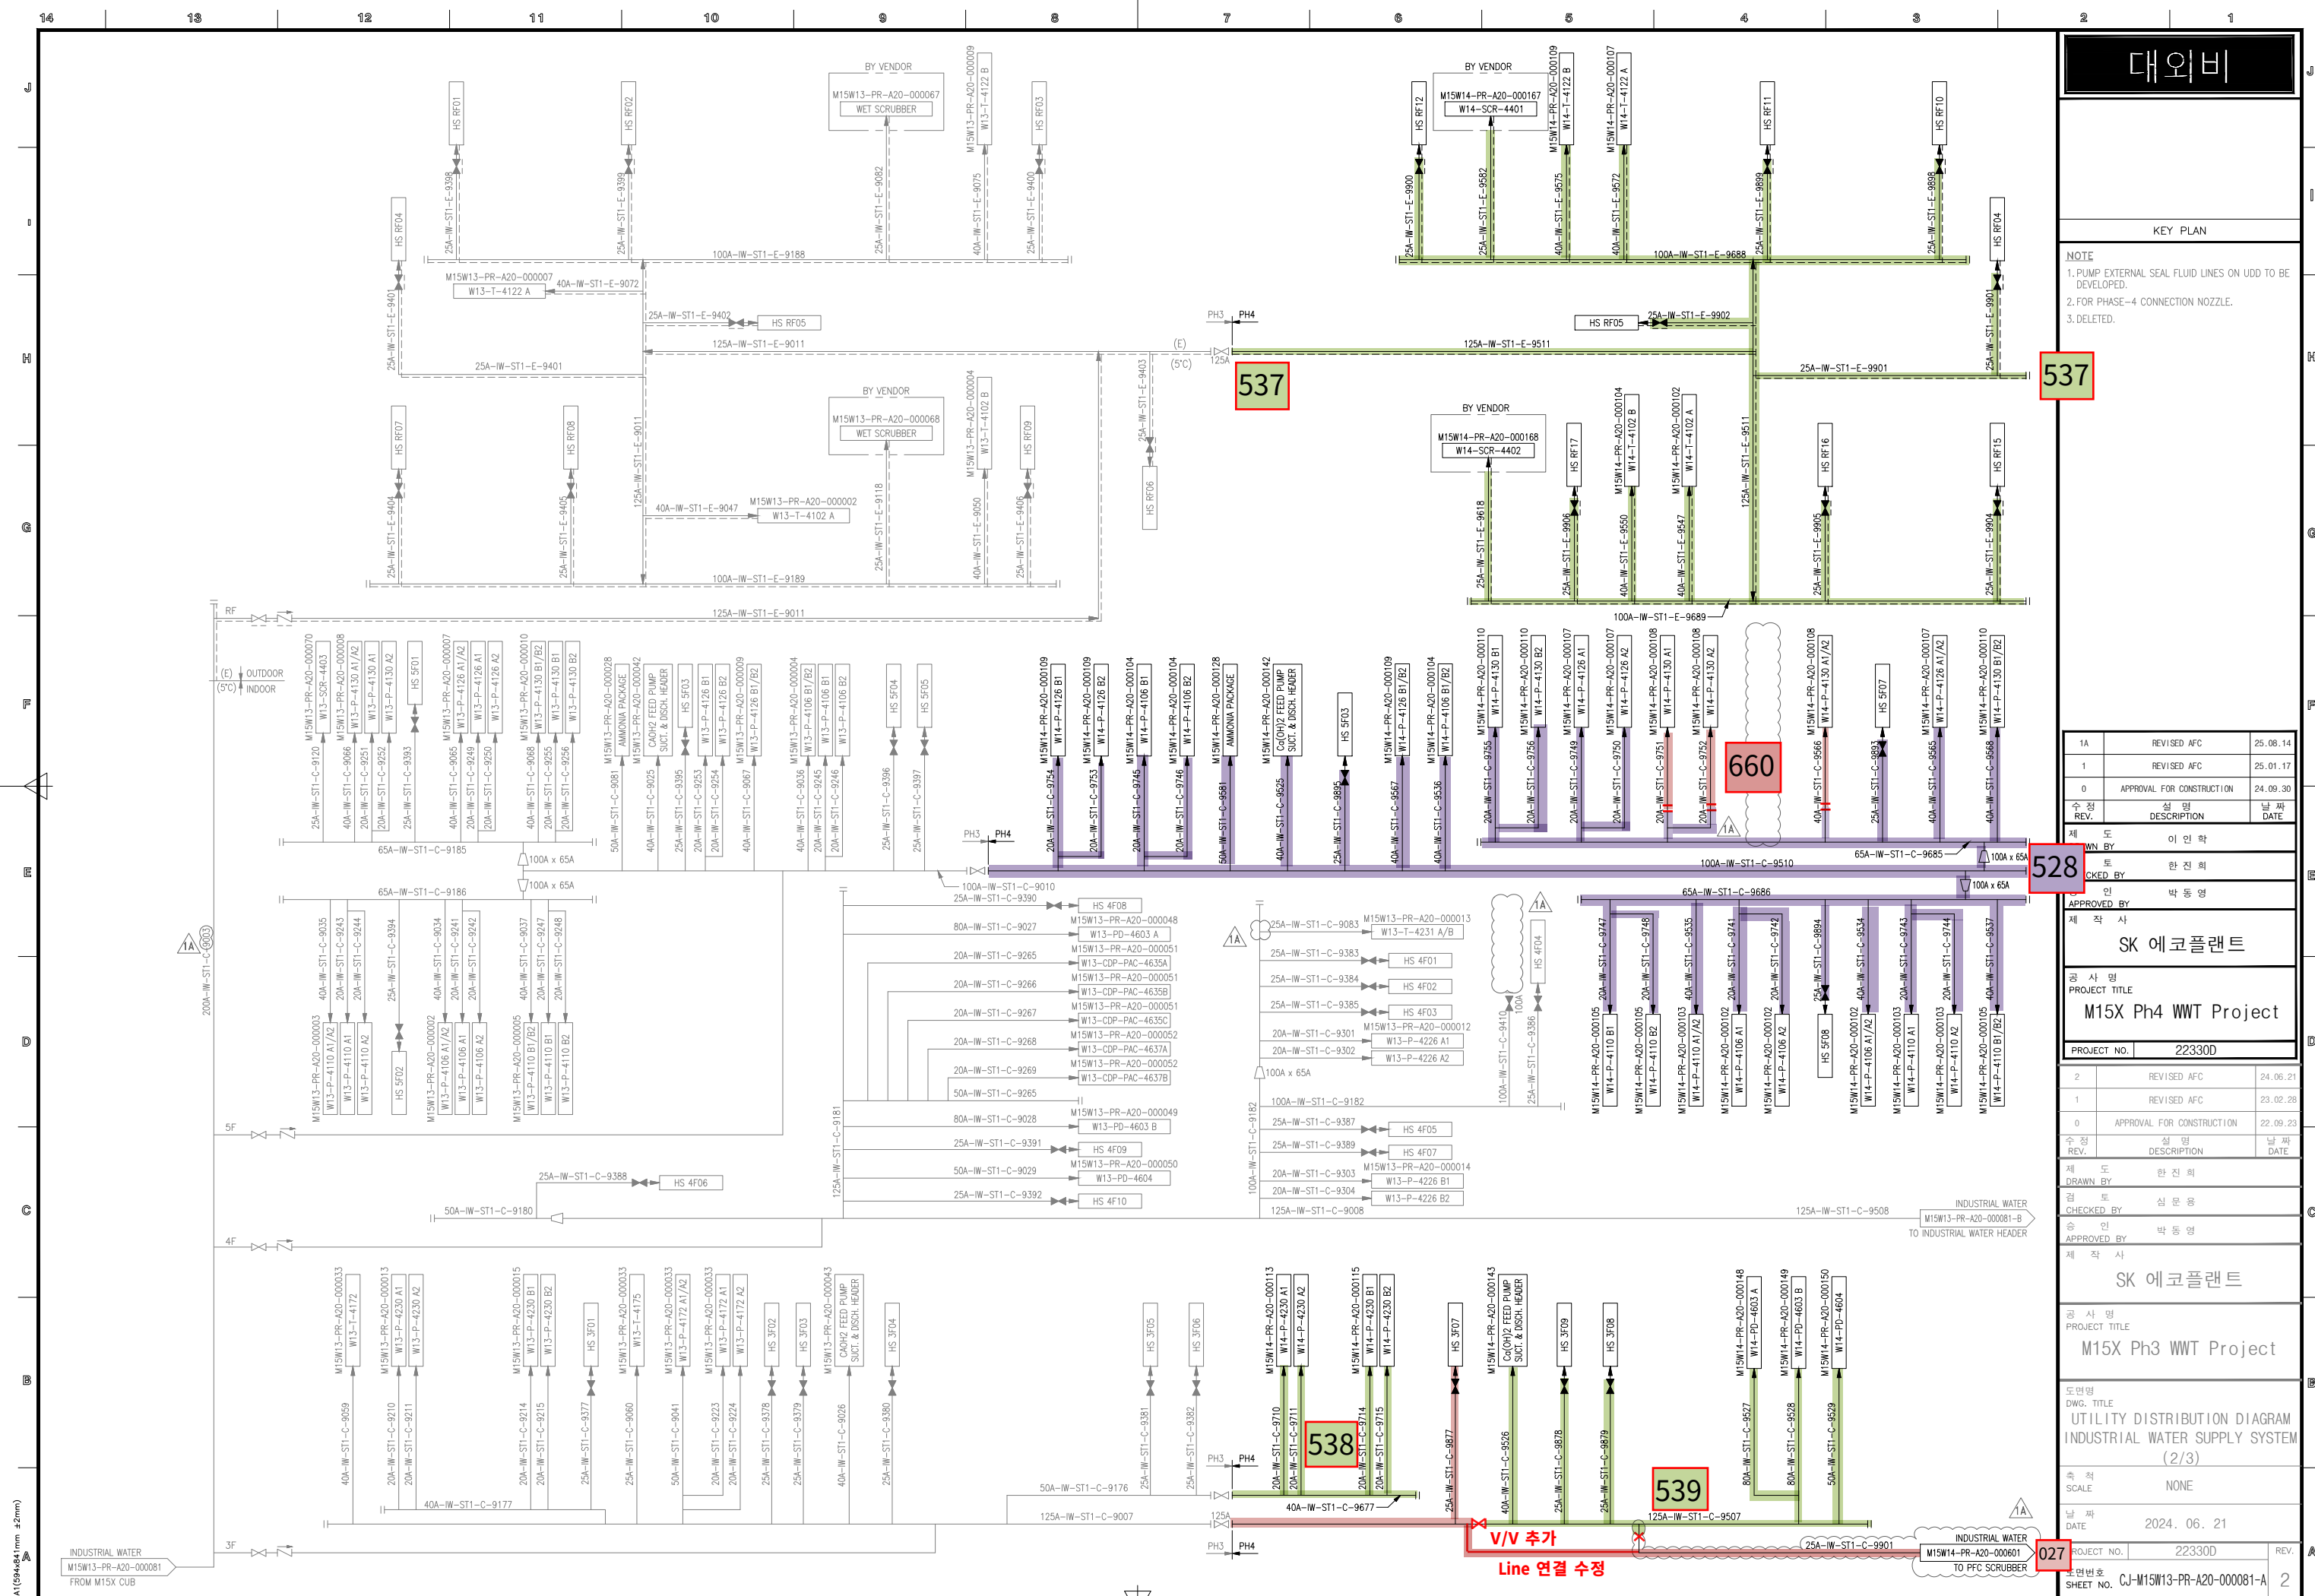


IW-660

PROJECT TITLE : M15X Ph2 Project[illegible]

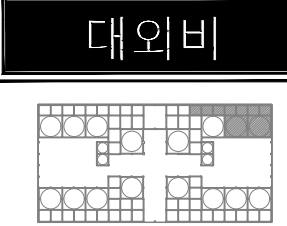

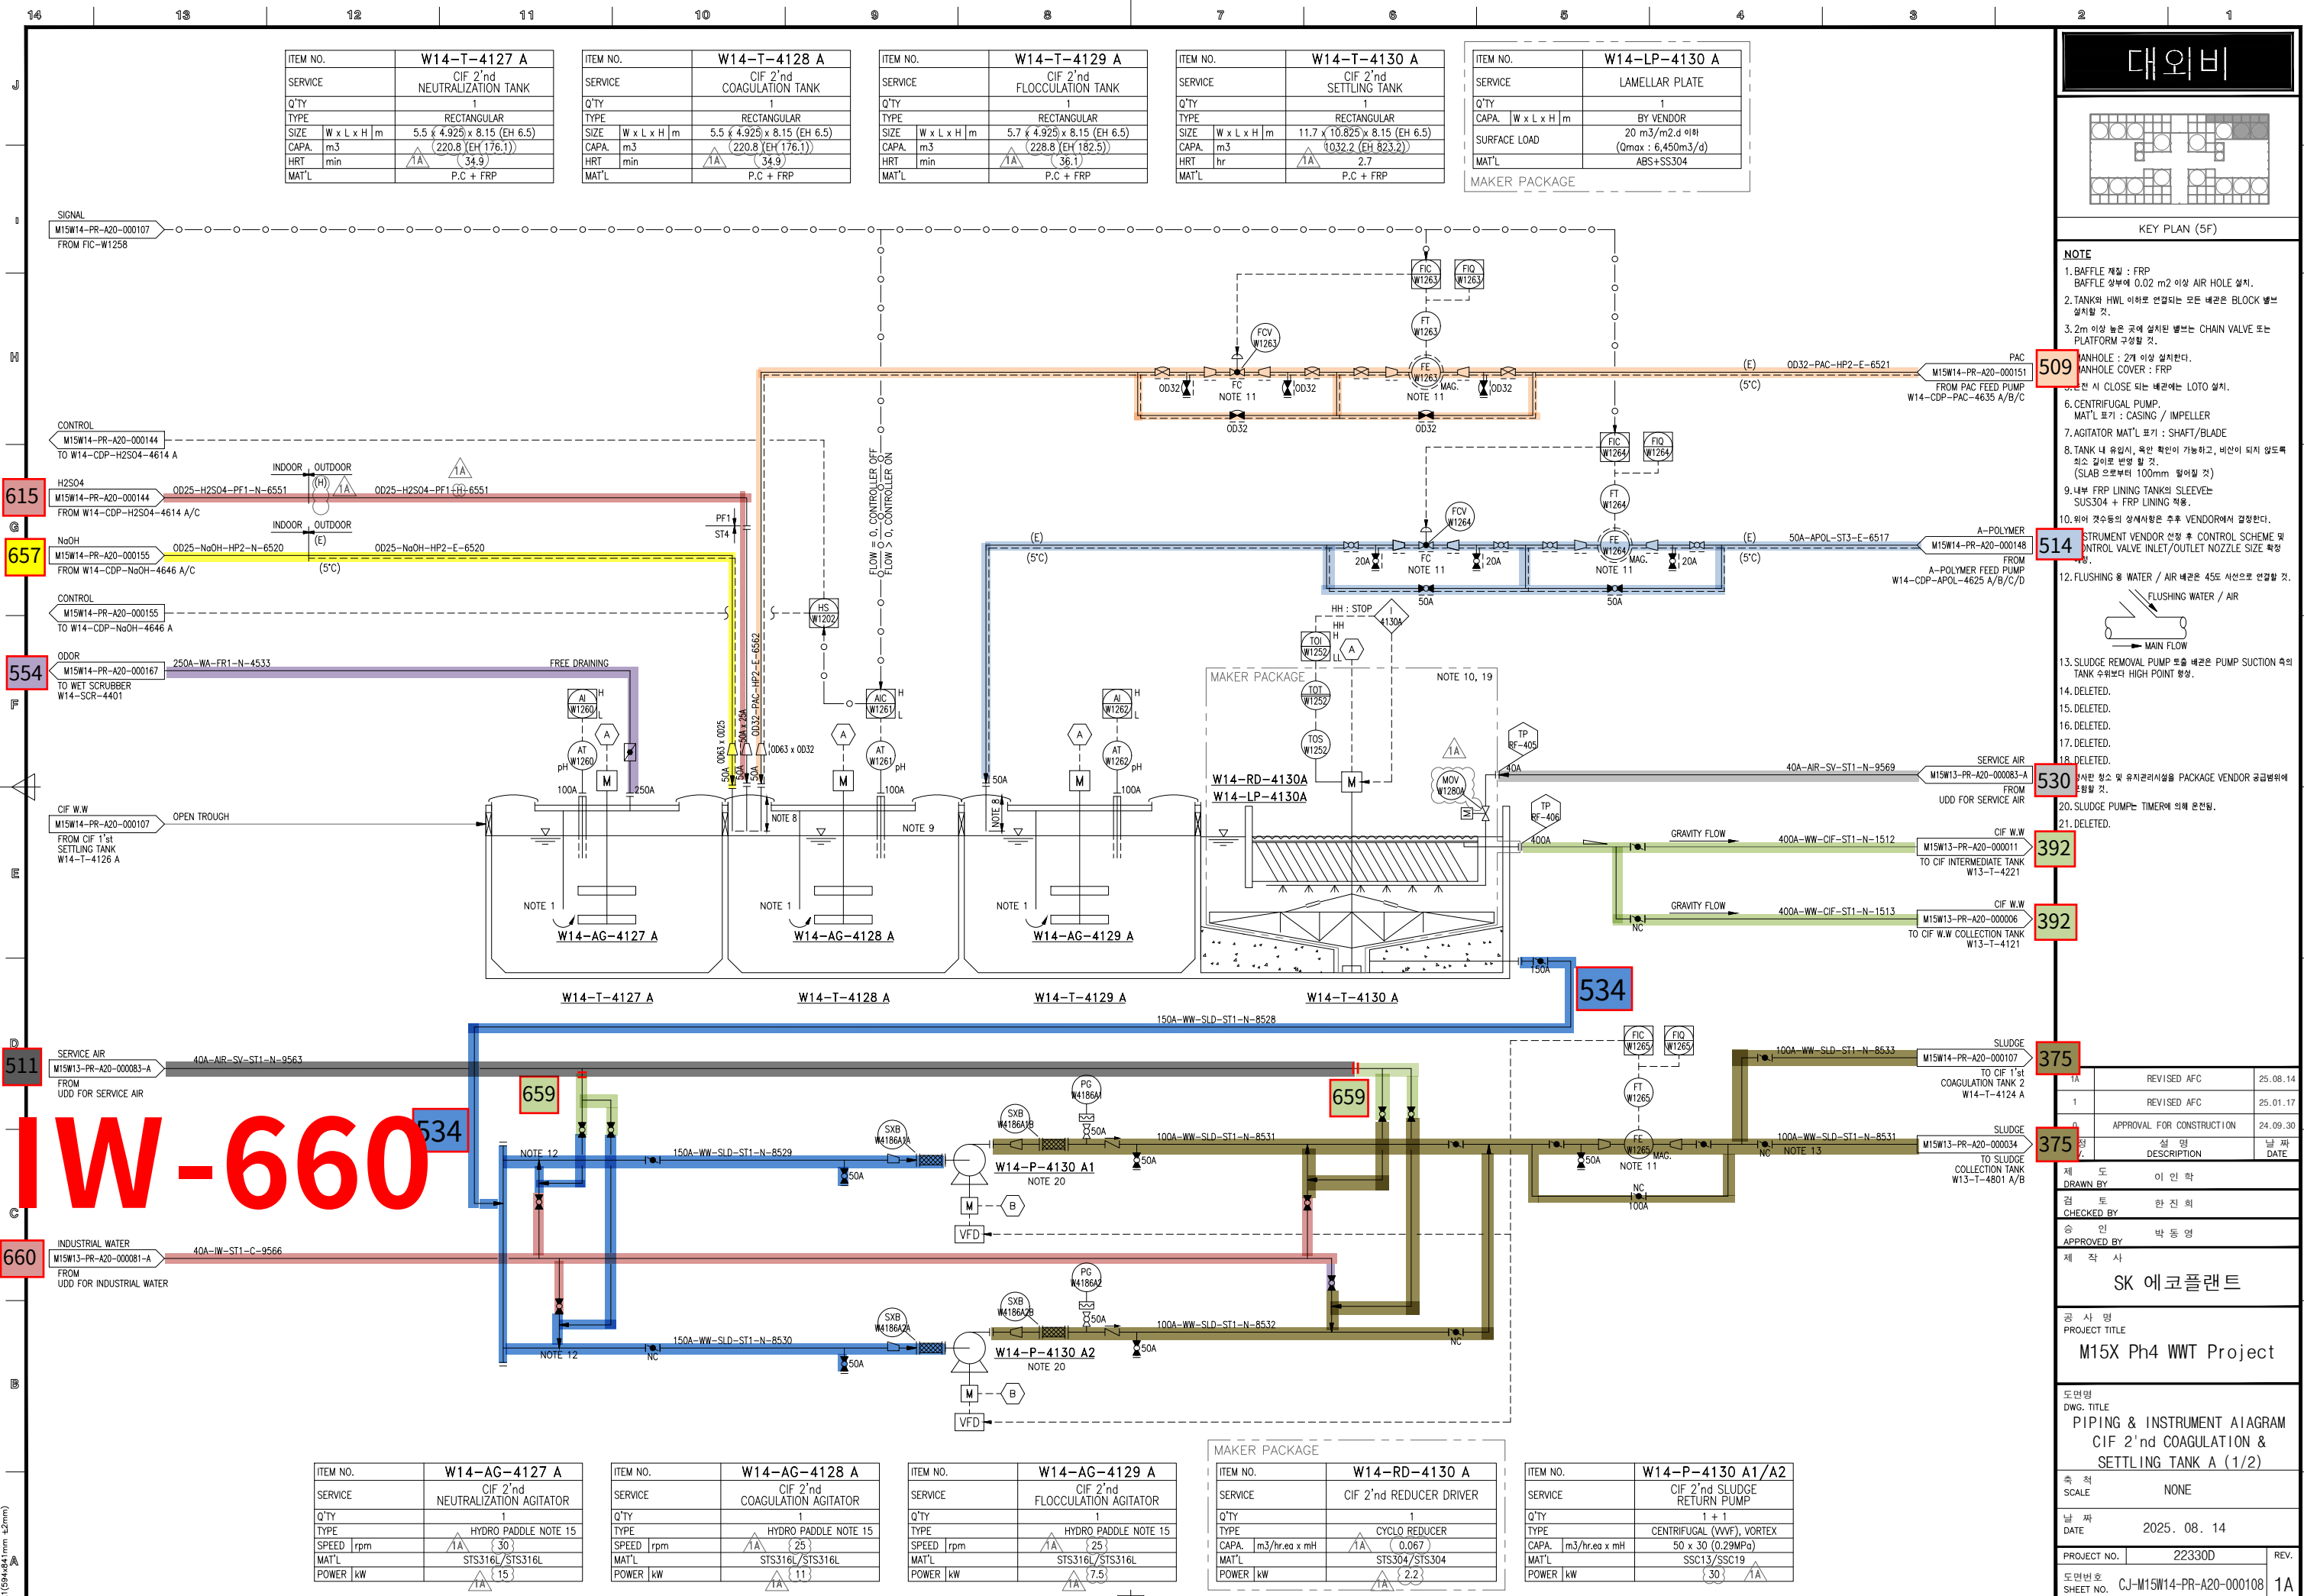

KEY PLAN (5F)

- NOTE**
1. Baffle 제형 : FRP
Baffle 상부에 0.02 m2 이상 AIR HOLE 설치.
 2. TANK의 HWL 이하로 연결되는 모든 배관은 BLOCK 밸브 설치할 것.
 3. 2m 이상 높은 곳에 설치된 밸브는 CHAIN VALVE 또는 PLATFORM 구성할 것.
 4. ANHOLE : 2개 이상 설치한다.
ANHOLE COVER : FRP
 5. 밸브 시 CLOSE 되는 배관에는 LOTO 설치.
 6. CENTRIFUGAL PUMP.
MAT'L 표기 : CASING / IMPELLER
 7. AGITATOR MAT'L 표기 : SHAFT/BLADE
 8. TANK 내 유입시, 육안 확인이 가능하고, 비산이 되지 않도록 최소 길이로 반영 할 것.
(SLAB 으로부터 100mm 떨어질 것)
 9. 내부 FRP LINING TANK의 SLEEVE는 SUS304 + FRP LINING 적용.
 10. 기타 특수등의 상세사항은 추후 VENDOR에서 결정한다.
 11. INSTRUMENT VENDOR 선정 후 CONTROL SCHEME 및 CONTROL VALVE INLET/OUTLET NOZZLE SIZE 확정
 12. FLUSHING 용 WATER / AIR 배관은 45도 서선으로 연결할 것.
 13. SLUDGE REMOVAL PUMP 또는 배관은 PUMP SUCTION 속의 TANK 수위보다 HIGH POINT 형성.
 14. DELETED.
 15. DELETED.
 16. DELETED.
 17. DELETED.
 18. DELETED.
 19. 시판 형소 및 유지관리시설을 PACKAGE VENDOR 공급범위에 포함할 것.
 20. SLUDGE PUMP는 TIMER에 의해 운전됨.
 21. DELETED.

1A	REVISED AFC	25.08.14
1	REVISED AFC	25.01.17
0	APPROVAL FOR CONSTRUCTION	24.09.30
375	실명	날짜
375	DESCRIPTION	DATE

제 도	이 인 학
DRAWN BY	
검 토	한 진 희
CHECKED BY	
승 인	박 동 명
APPROVED BY	
제 작 사	

SK 에코플랜트

공 사 명

PROJECT TITLE

M15X Ph4 WWT Project

도면명

DWG. TITLE

PIPING & INSTRUMENT DIAGRAM

CIF 2'nd COAGULATION & SETTLING TANK A (1/2)

속 척

SCALE

NONE

날 짜

DATE

2025. 08. 14

PROJECT NO.


22330D

도면번호

SHEET NO.

CJ-M15W14-PR-A20-000108

1A

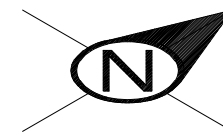

<NOTE>
1. (*) FIELD ADJUST

CLIENT 


INSULATION	CODE	C	CONDITION	PRESS. (kg/cm2g)	TEMP. (°C)	AREA W14						
	THICK.	25	DESIGN	13.5	60	UNIT 5FA						
			OPERATING	10	AMB	REF. PLAN DWG. CJ-M15W14-PI-A30-050004-D		25.01.24	APPROVED FOR CONSTRUCTION	황래중	안남후	박동영
						REF. P & ID CJ-M15W14-PR-A20-000108						

CONTRACTOR		PROJECT NAME	
		M15X Ph4 Project	
COMMODITY		JOB NO.	
IW		22330D	
LINE NO.	SH'T NO.	REV.	
40A-IW-ST1-C-9566	01 / 02	0	

경고 : 본 도면은 SK HYNIX의 기업비밀 자료로서, 어떠한 경우에도 목적 외 사용, 복제, 제3자에게 공개, 누설 및 유출할 수 없으며, 회사는 유포자의 불법 사용으로 피해가 발생할 경우 유포자에게 민/형사상 책임을 요구할 수 있음



ITEM	SIZE	Q'TY	DESCRIPTION
ST1			
P	40A	7.0M	PIPE, STS 304TP, ERW, PE – SCH 10S
E90	40A	4EA	ELBOW 90 DEG, STSF304, SW – SCH 10S
E45	40A	1EA	ELBOW 45 DEG, STSF304, SW – SCH 10S
T	40A	3EA	TEE EQUAL, STSF304, SW – SCH 10S
VB	40A	2EA	BALL VALVE, KS 10K, RF FLG'D, BODY–STSF304 /
			TRIM–ST304 / SEAT–PTFE, FB, LEVER
F	40A	6EA	FLG SO, KS 10K, RF, STS304
G	40A	4EA	GASKET, KS 10K, RF, PTFE+EPDM, 3.0MM TH'K
B	40A	4SET	MACHINE BOLT & NUTS :STS 304 / W WASHERS
IN	25tX40A	7.0M	관 보존재(고무발포)

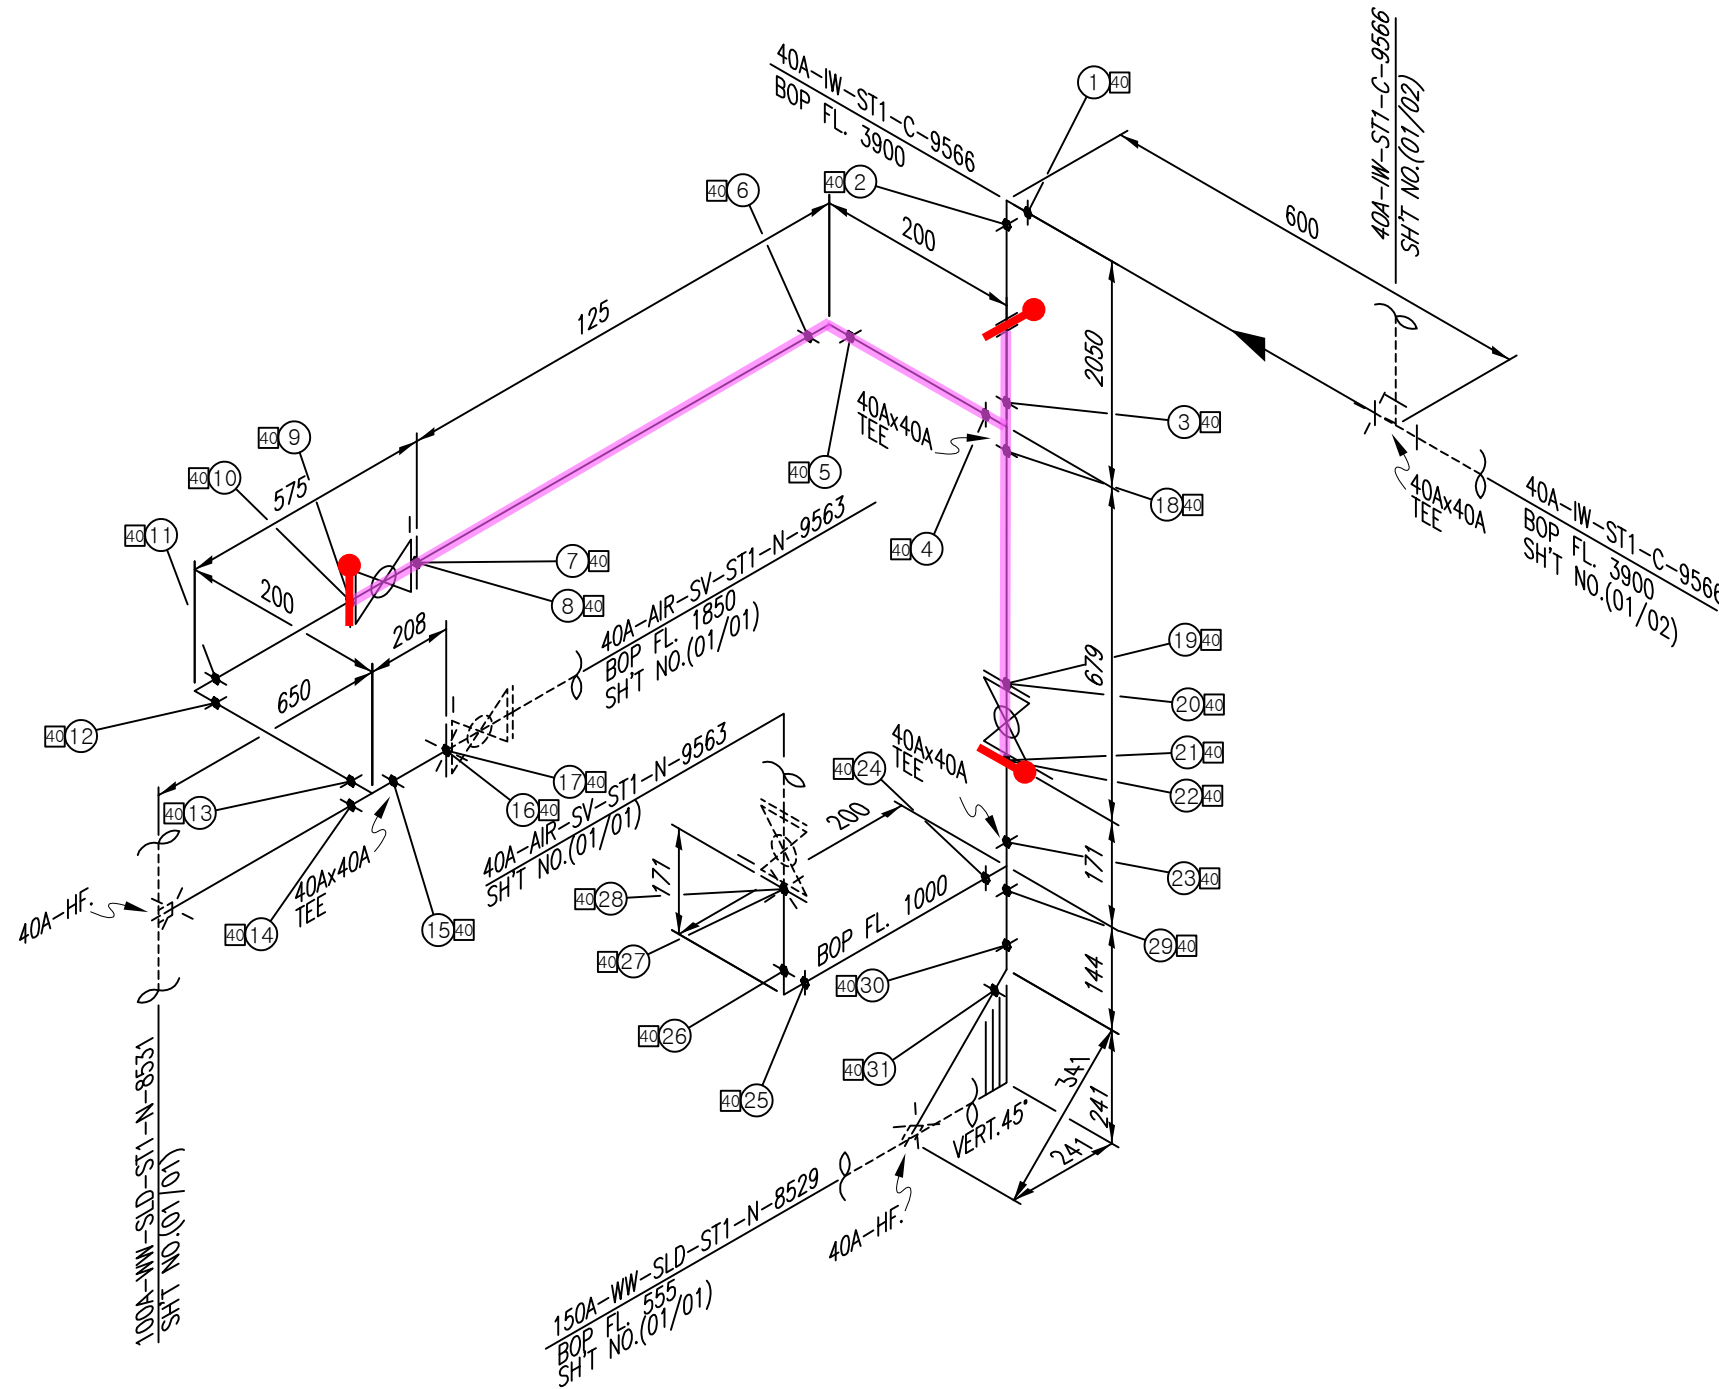

<NOTE>

1. (*) FIELD ADJUST

* PIPE : P/P1	* 90° ELBOW : E90	* 45° ELBOW : E45	* TEE : T	* RED.TEE : TR	* STUB-IN : STU	* REINFORCING PAD : RP	* CON.RED : RC	* ECC.RED : RE	* CON.SWAGE : RCS/RCS1	* ECC.SWAGE : RES/RES1	* NIPPLE : NP/NP1/NP2	* CAP : CAP/CAP1	* PLUG : PLG	* FULL COUPLING : FC	* HALF COUPLING : HF/HF1
* STUB-IN : STU	* SOCKET(HDPE/PVC) : SC	* SADDLE(HDPE) : SD	* FLANGE : F/F1	* GASKET : G/G1/G2	* BOLT & NUT : B/B1	* BLIND FLANGE : FB/FB1	* GATE VA. : VG/VG1/VG2	* BALL VA. : VB/VBLO/VB1/VBLO/VB2/VB2LO	* BUTTERFLY VA. : VF/VF4	* CHECK VA. : VC/VC1/VC2/VC3/VC4/VC5/VC6/VC7					
* GLOBE VA. : VL/VL1/VL2	* DIAPHRAGM VA. : VD/VDLO	* DAMPER : VP	* QUICK COUPLING : SQC	* FLEXIBLE JOINT(STEEL) : FLXB	* FLEXIBLE JOINT(RUBBER) : FLXR	* FLEXIBLE JOINT(STEEL PTFE LINED) : FLXL	* FLEXIBLE HOSE : FLXH	* STEAM TRAP : ST	* SPRAY NOZZLE : SPN	* EMERGENCY SHOWER : SSH					
* STRAINER(Y-TYPE) : YSTR	* STRAINER(T-TYPE) : TSTR	* STRAINER(BUCKET-TYPE) : BSTR	* ANCHOR PLATE : STOP	* BIRD SCREEN : BS	* ISOLATION KIT : IK	* UNLOADING BOX : UB	* AIR TRAP : AT	* LOTO : LOTO	* SIGHT GLASS : SG	* PRESSURE GAUGE : PG	* SHILED : SH	* SPECIAL BOLT & NUT : BL/BL1			

INSULATION	CODE	C	CONDITION	PRESS. (kg/cm2g)	TEMP. (°C)	AREA	W14							CONTRACTOR	PROJECT NAME	
	THICK.	25	DESIGN	13.5	60	UNIT	5FA								M15X Ph4 Project	
			OPERATING	10	AMB	REF. PLAN DWG.								COMMODITY	JOB NO.	
						CJ-M15W14-PI-A30-050004-D			25.01.24	APPROVED FOR CONSTRUCTION	황래중	안남후	박동영	IW	22330D	
						REF. P & ID		REV. NO.	DATE	DESCRIPTION	BY	CHK	APP'D	LINE NO.	SH'T NO.	REV.
						CJ-M15W14-PR-A20-000108								40A-IW-ST1-C-9566	02 / 02	0

[illegible]



CONTRACTOR		PROJECT NAME	M15X Ph4 Project
COMMODITY	IW	JOB NO.	22330D
LINE NO.	20A-IW-ST1-C-9752	SH'T NO.	01 / 01
		REV.	0

INSULATION	CODE	C	CONDITION	PRESS. (kg/cm2g)	TEMP. (°C)	AREA	W14						
	THICK.	25	DESIGN	13.5	60	UNIT	5FA						
			OPERATING	10	AMB	REF. PLAN DWG. CJ-M15W14-PI-A30-050004-D							
						REF. P & ID CJ-M15W14-PR-A00-000011			25.01.24	APPROVED FOR CONSTRUCTION	황래중	안남후	박동영
								REV. NO.	DATE	DESCRIPTION	BY	CHK	APP

경고 : 본 도면은 SK HYNIX의 기밀비밀 자료로서, 어떠한 경우에도 목적 외 사용, 복제, 제3자에게 공개, 누설 및 유출할 수 없으며, 회사는 유포자의 불법 사용으로 피해가 발생할 경우 유포자에게 민/형사상 책임을 요구할 수 있음.